

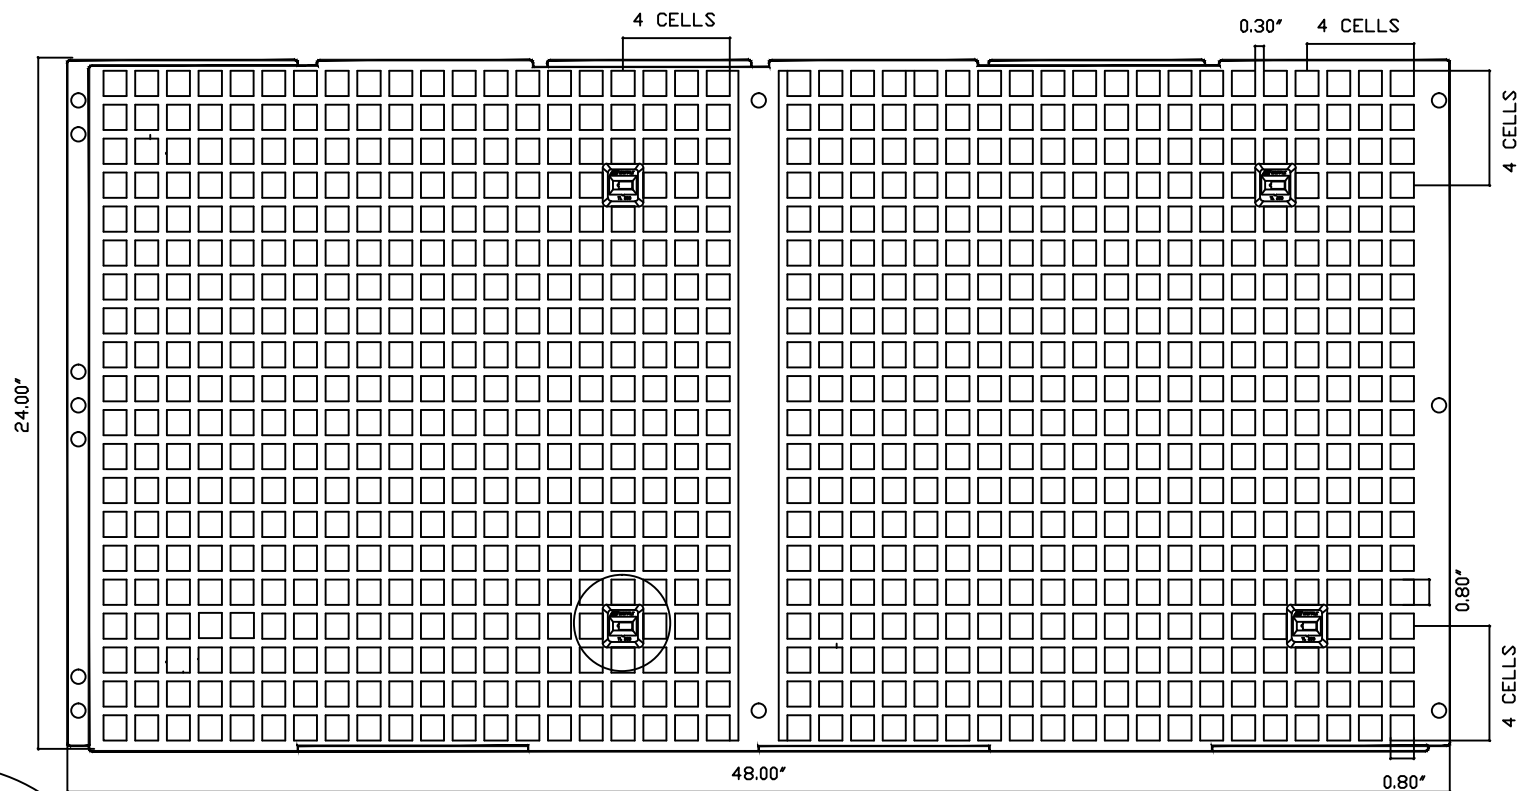


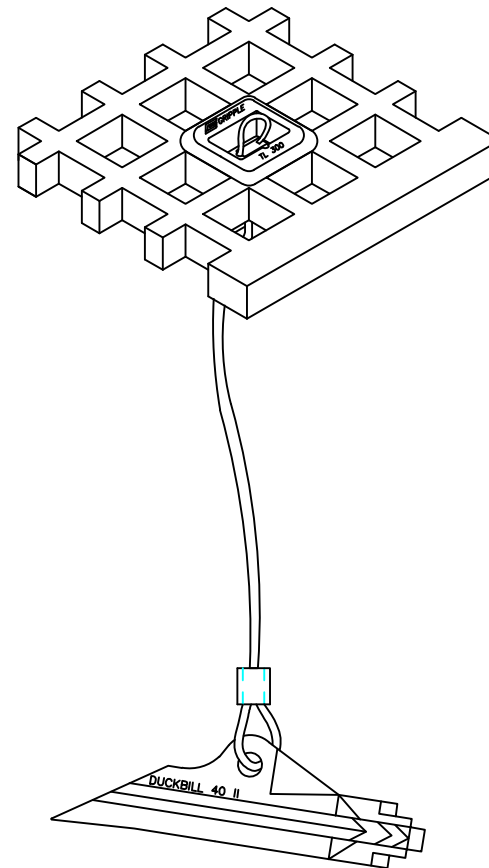

ANCHOR DETAIL

NOTE: THE ACTUAL NUMBER & LOCATIONS
WILL BE DETERMINED BY VEHICLE LOADING
AND SUB GRADE TYPE

		PRESTO® PRODUCTS CO. 670 NORTH PERKINS STREET APPLETON, WI 54914 920-738-1342 WWW.PRESTOGEO.COM	
GEORUNNER FLOW PROTECTION SYSTEM			
PRESTO®, GEOSYSTEMS®, AND GEORUNNER® ARE REGISTERED TRADEMARKS OF PRESTO PRODUCTS.			
DATE	DECEMBER 2017	FILE NAME	GEORUNNER Anchor
SCALE	NTS	SHEET	1 OF 1

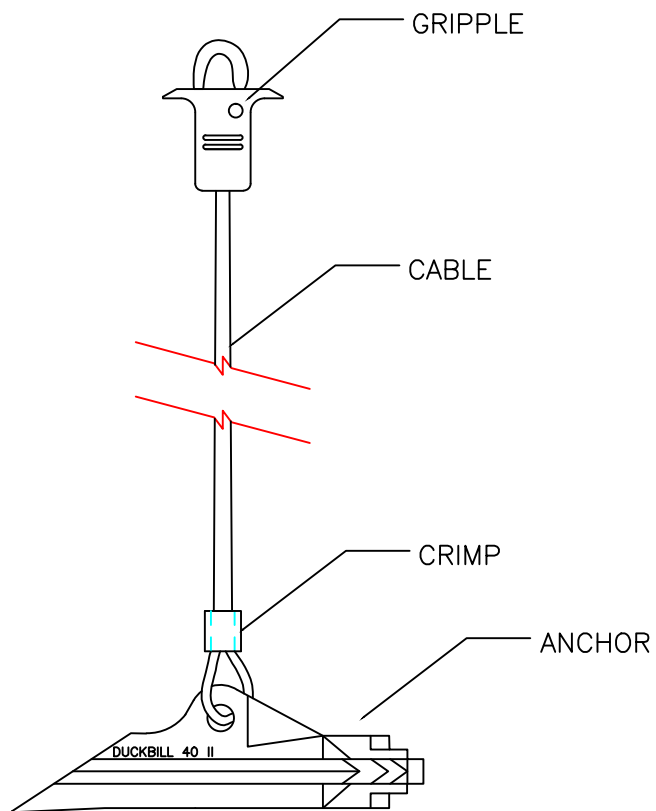

		PRESTO® PRODUCTS CO. 670 NORTH PERKINS STREET APPLETON, WI 54914 920-738-1342 WWW.PRESTOGEO.COM	
GEOSYSTEMS			
GEORUNNER ANCHOR DETAIL			
PRESTO®, GEOSYSTEMS®, AND GEORUNNER® ARE REGISTERED TRADEMARKS OF PRESTO PRODUCTS.			
DATE	DECEMBER 2017	FILE NAME	GEORUNNER Anchor Det
SCALE	NTS	SHEET	1 OF 1